

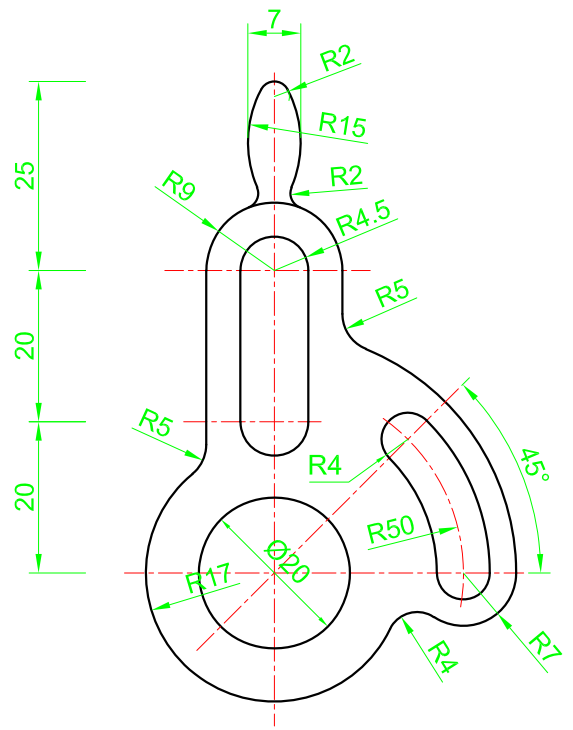


一、绘制平面图，并标注尺寸。

二、绘制平面图，并标注尺寸。

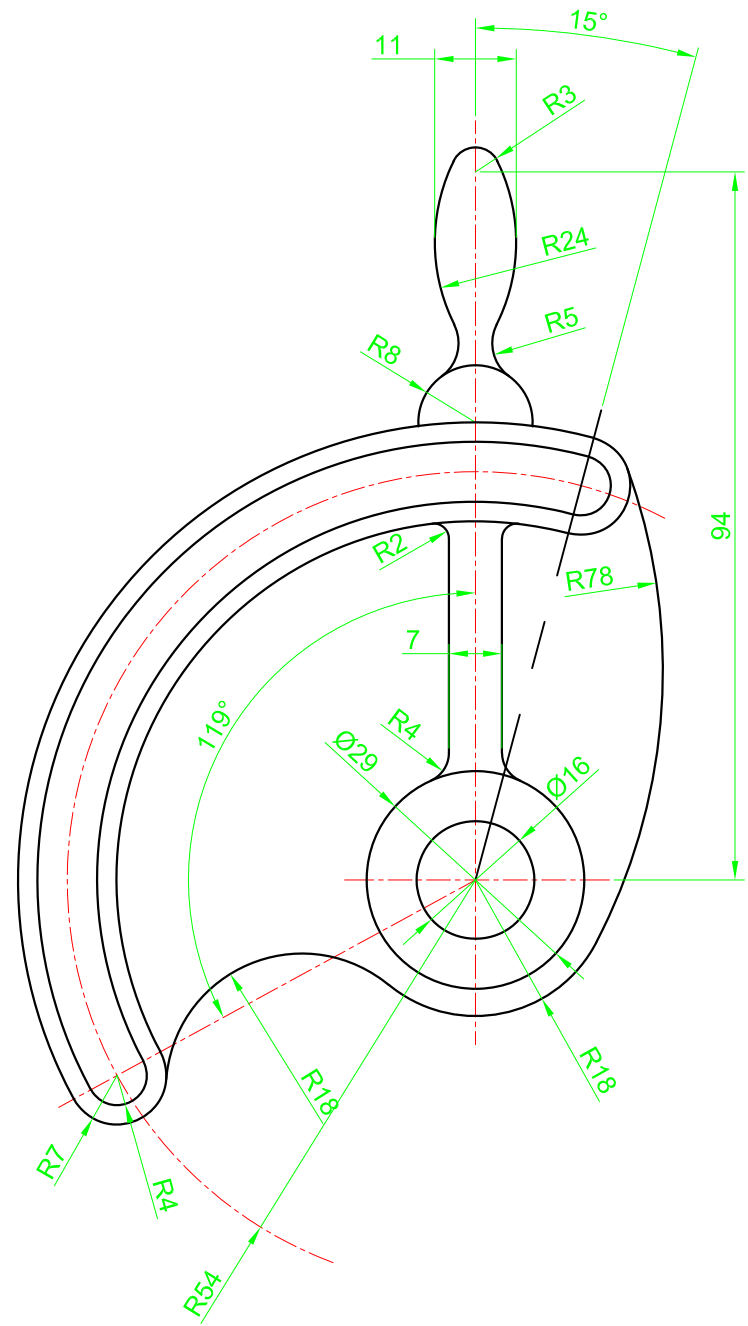

三、绘制下面的主视图和俯视图，并画出左视图、标注尺寸。

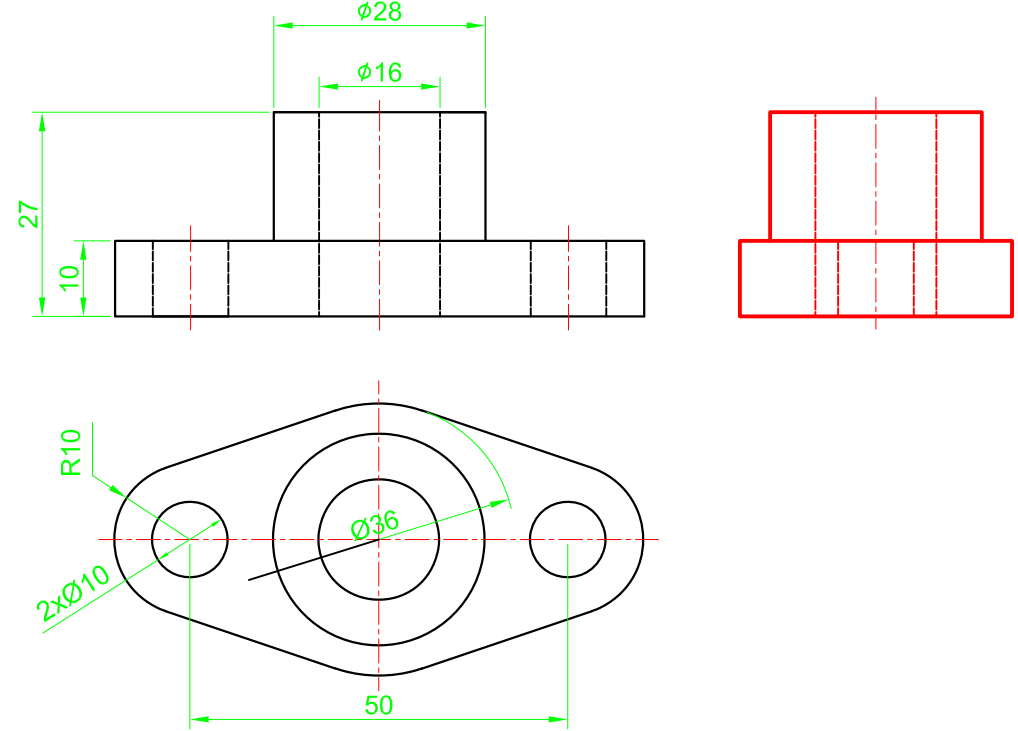

图层	颜色	线型	线宽
图框 标题栏外框	白/黑	Continuous	0.5000
点划线	红	Center	0.3000
尺寸标注	绿	Continuous	0.3000
轮廓线	白/黑	Continuous	0.5000
细实线	白/黑	Continuous	0.3000
虚线	白/黑	Dashed	0.3000
标题栏文字	青	Continuous	0.3000
表格及表格文字	蓝	Continuous	0.3000

期末练习		比例	数量	图号	得分
		1:1	3	1	
制图	张三	中山大学			
审核	张三				
学号	12345678				